
Cellar-Floor

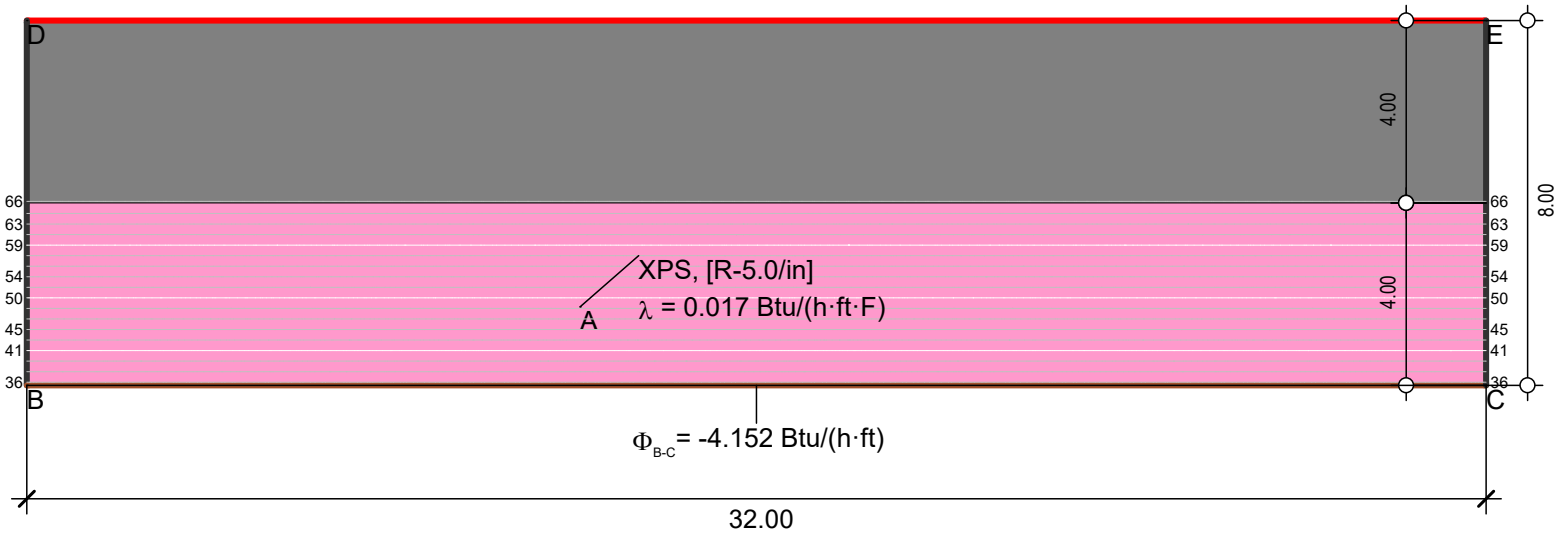

$$U_{eq\ B\text{-}C} = \frac{4.152}{32.94 \cdot 2.667} = 0.0473\ \text{Btu/(h·ft}^2\text{·F)} = \text{R-21.1416}$$

Boundary Condition	θ[°F]	h[Btu/(h·ft²·F)]
Exterior, Pittsburgh 90d Avg, Soil	35.060	
Interior, heat flux, downwards	68.000	1.036
Symmetry/Model section		

Material	λ[Btu/(h·ft·F)]	ε
Concrete (Heavily Reinforced) [R-0.05/in]	1.733	0.900
XPS, [R-5.0/in]	0.017	0.900