
Cellar-Wall

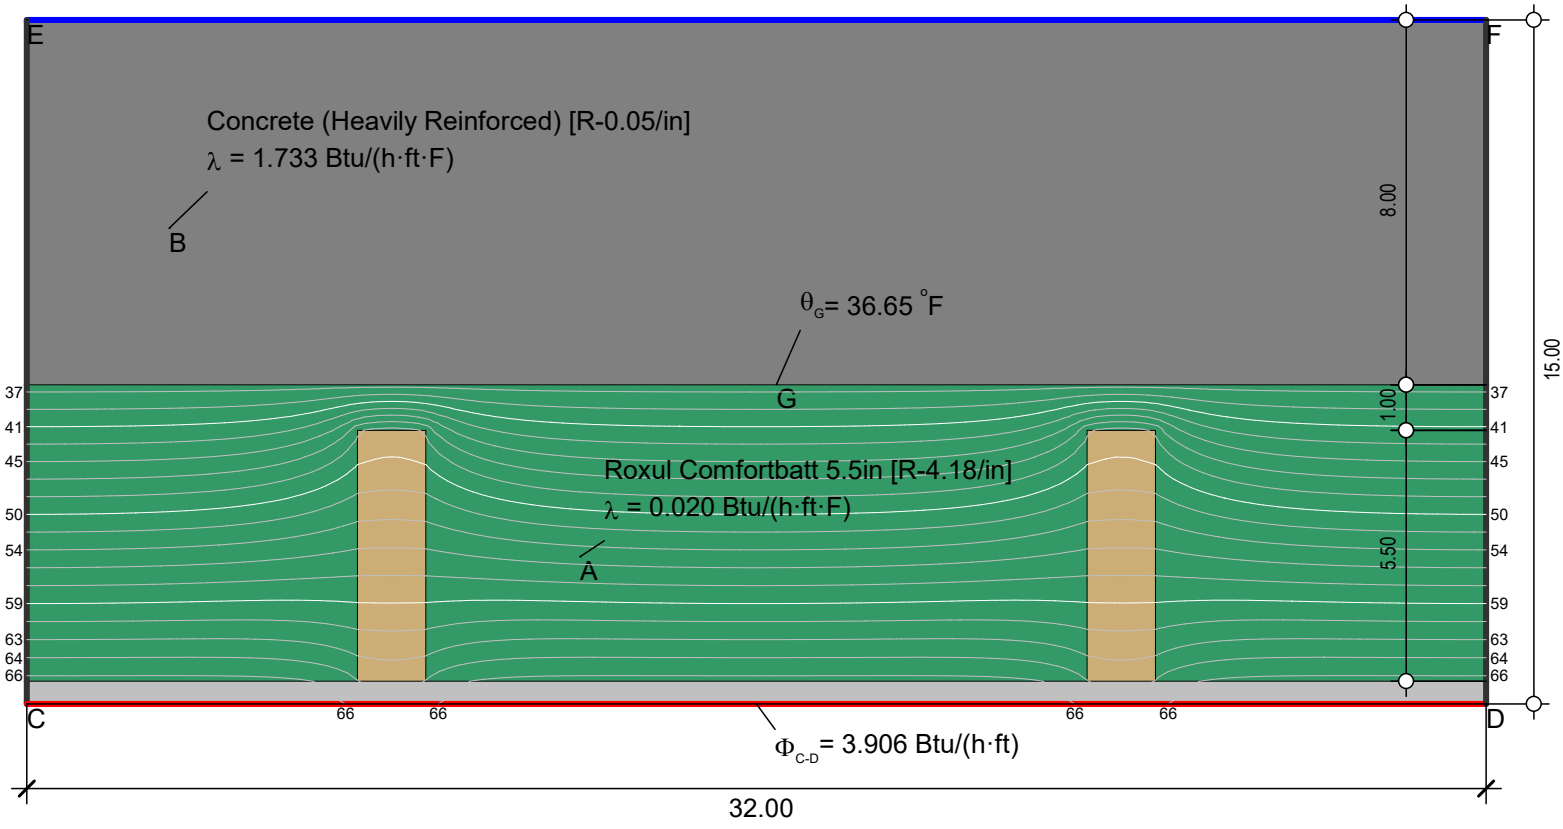

$$U_{eq\ C\text{-}D} = \frac{3.906}{32.94 \cdot 2.667} = 0.0445\ \text{Btu/(h·ft}^2\text{·F)} = \text{R-22.4719}$$

Boundary Condition	θ[°F]	h[Btu/(h·ft²·F)]
Exterior, Pittsburgh 90d Avg	35.060	1.355
Interior, normal, horizontal	68.000	1.355
Symmetry/Model section		

Material	λ[Btu/(h·ft·F)]	ε
Concrete (Heavily Reinforced) [R-0.05/in]	1.733	0.900
GWB (Typ) [R-0.85/in]	0.098	0.900
Roxul Comfortbatt 5.5in [R-4.18/in]	0.020	0.900
Wood, Coniferous [550 kg/m3], grain vertical	0.071, 0.161	0.900