
Exposed-Floor

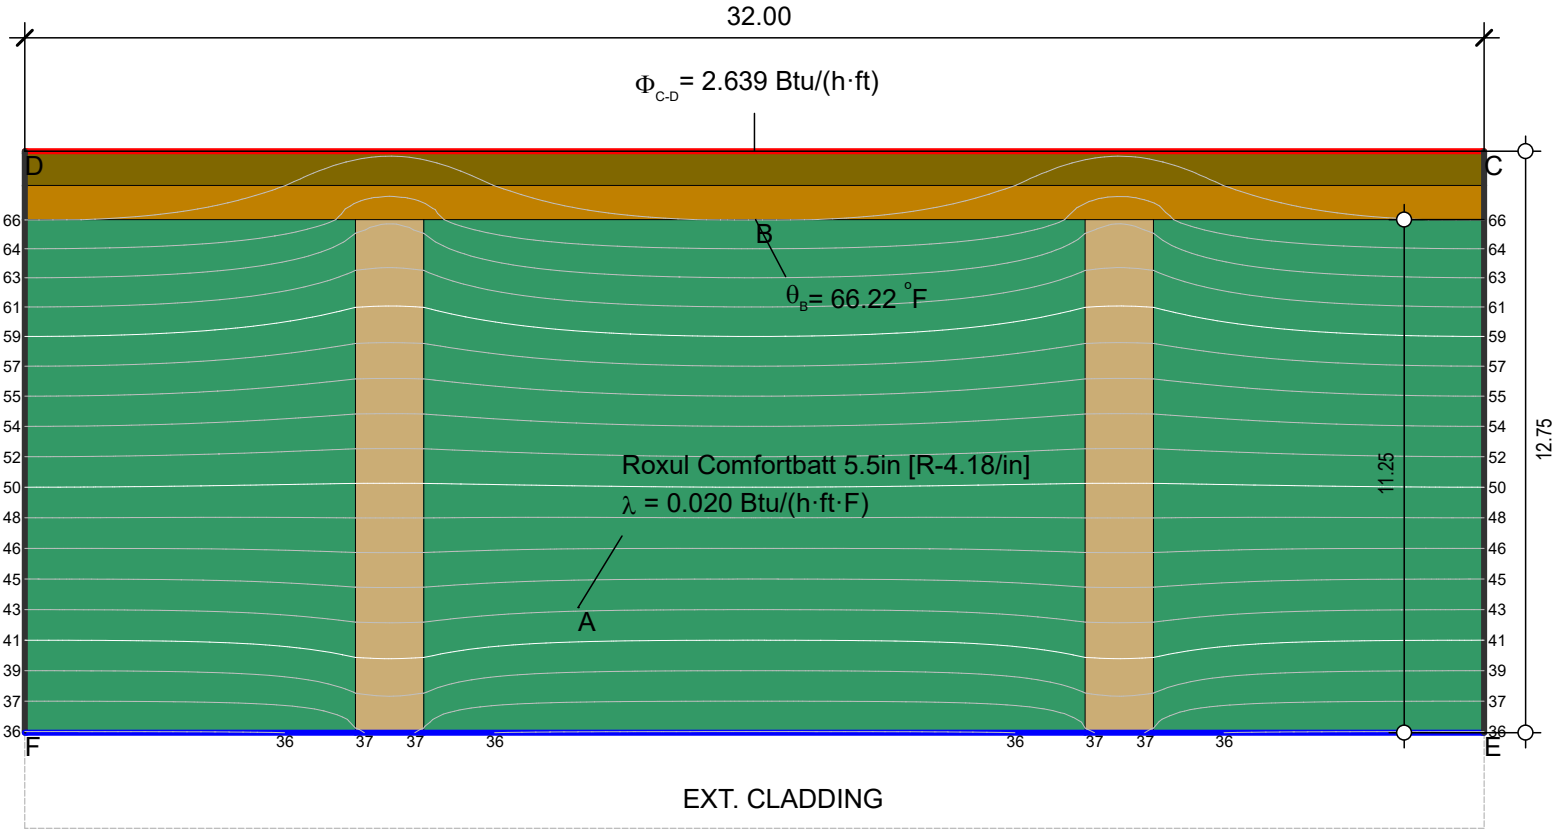

$$U_{eq\ C\text{-}D} = \frac{2.639}{32.94 \cdot 2.667} = 0.0300\ \text{Btu/(h·ft}^2\text{·F)} = \text{R-33.3333}$$

Boundary Condition	θ[°F]	h[Btu/(h·ft²·F)]
Exterior, Pittsburgh 90d Avg	35.060	1.355
Interior, heat flux, downwards	68.000	1.036
Symmetry/Model section		

Material	λ[Btu/(h·ft·F)]	ε
Plywood (Typ) [R-1.2/in]	0.069	0.900
Roxul Comfortbatt 5.5in [R-4.18/in]	0.020	0.900
Wood, Coniferous [550 kg/m3], grain vertical	0.071, 0.161	0.900
Wood, Deciduous (Hardwood) [R-0.91/in]	0.092	0.900