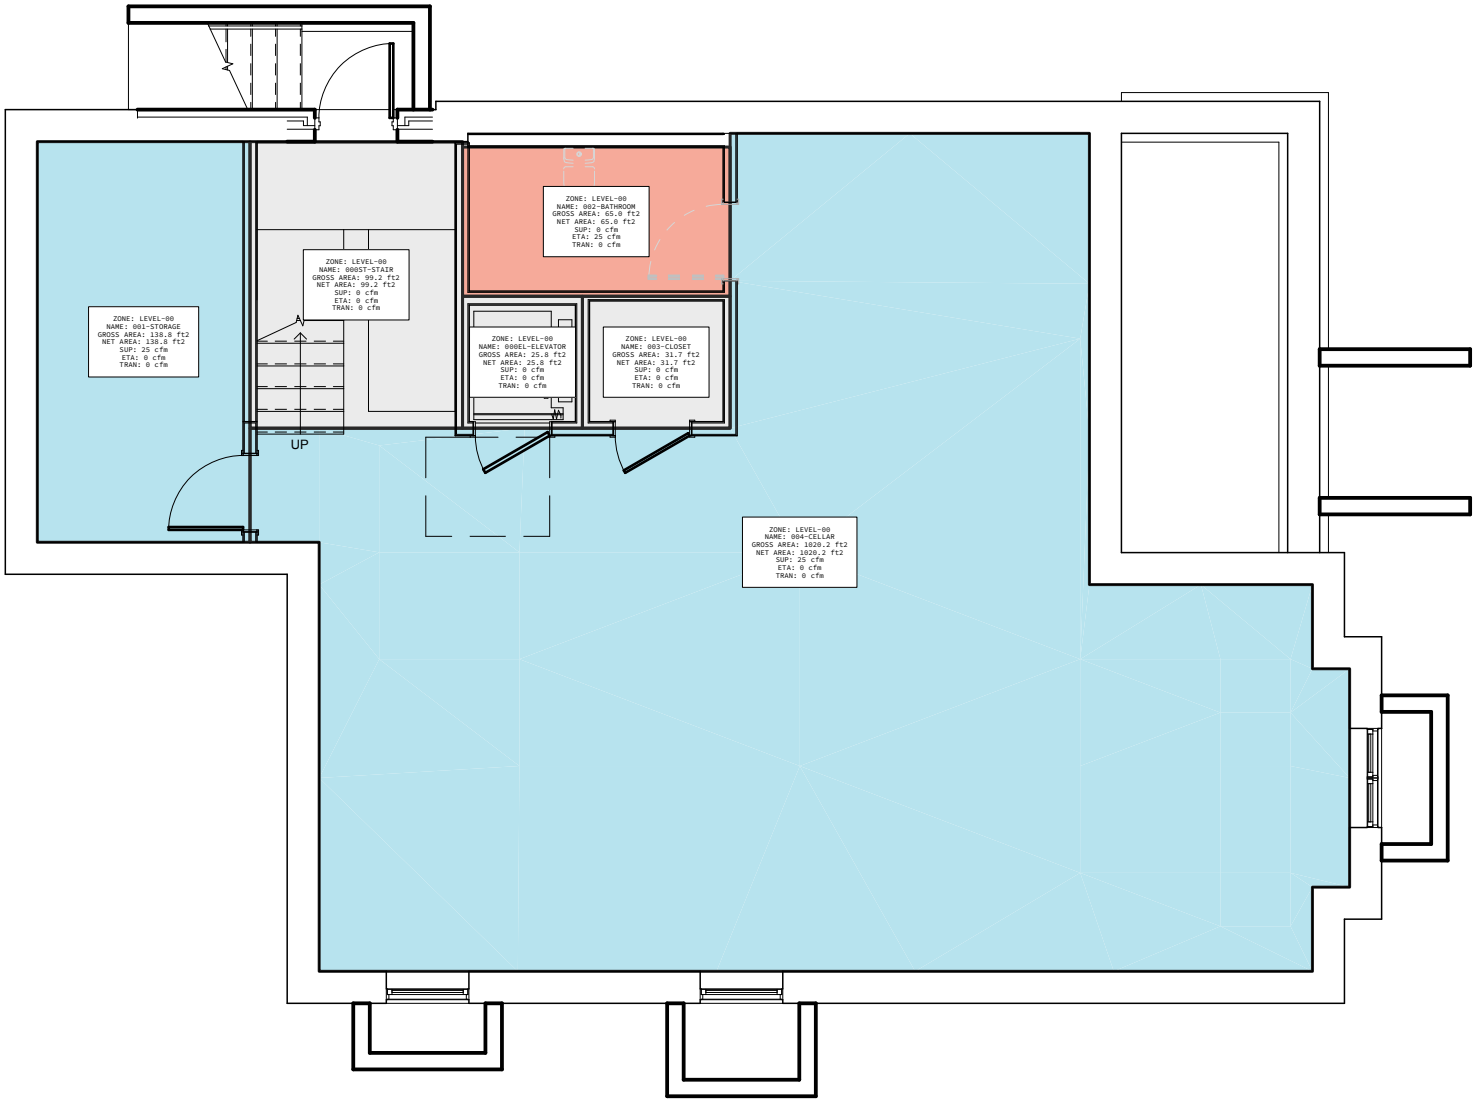


WATERMAN HOUSE

FRESH-AIR VENTILATION PLANS

Ventilation:

SUPPLY | EXTRACT | SUP & ETA

OCT. 26, 2026